

Site Plan

Front Point Properties & Construction (Design)

GENERAL NOTES

Drawing Interpretation:
All dimensions are in millimeters (mm) unless otherwise noted.
Discrepancies between drawings shall be reported to the architect for clarification.

Drawing Revisions:
Always refer to the latest revision. Obsolete drawings must not be used.

Coordination:
All disciplines (Architectural, Structural, MEP) must be cross-referenced for conflicts.
Report clashes between services (e.g., ductwork vs. structural beams) immediately.

Site Verification:
Contractor must verify all dimensions on-site before construction.

ARCHITECTURAL

All finishes shall be as per the Finishes Schedule and Material Specifications.
Mock-ups of critical finishes (e.g., façade, flooring) must be approved before full installation.
Compliance:
Construction shall comply with local building codes, accessibility standards (e.g., ADA/ANSI), and fire regulations.
Tolerances:
Construction tolerances shall not exceed ±5mm unless otherwise specified.

STRUCTURAL

Design Standards:
Concrete, steel, and reinforcement shall comply with ACI 318, AISC, or local codes.
Loads:
All dead/live loads are as per ASCE 7 (or relevant standard). Unauthorized additional loads are prohibited.
Reinforcement:
Bar bending schedules (BBS) must be approved before fabrication.

SANITARY


Piping:
Use PVC/CPVC/GI as specified. Slope for drainage pipes: 2% minimum.
Water Supply:
Pressure test all pipes at 1.5× working pressure before concealment.
Fixtures:
Locations are indicative; confirm with architectural layouts.
Grease Traps & Interceptors:
Install as per local sanitary codes.

ELECTRICAL


Standards:
Installation shall comply with NEC/IEC (or local electrical code).
Coordination:
Conduits and cable trays must avoid clashes with plumbing/mechanical ducts.
Fixtures:
Lighting layouts are schematic; final positions to be confirmed with architect.
Earthing & Safety:
All systems must include proper grounding and surge protection.

MECHANICAL

Ductwork:
Install as per SMACNA standards. Fire dampers required at rated walls.
Equipment:
AHUs, chillers, and fans shall be as per manufacturer's specifications.
Insulation:
All ductwork in unconditioned spaces must be insulated.

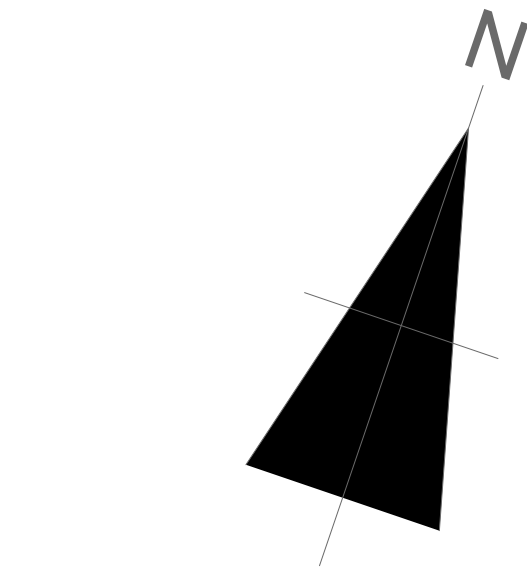

LAND USE ANALYSIS	
TOTAL LAND AREA	292.17M ²
BUILT UP AREA	115.69M ²
UNBUILT AREA	176.48M ²
% BUILT UP AREA	39.60%
%UNBUILT AREA	40.40%

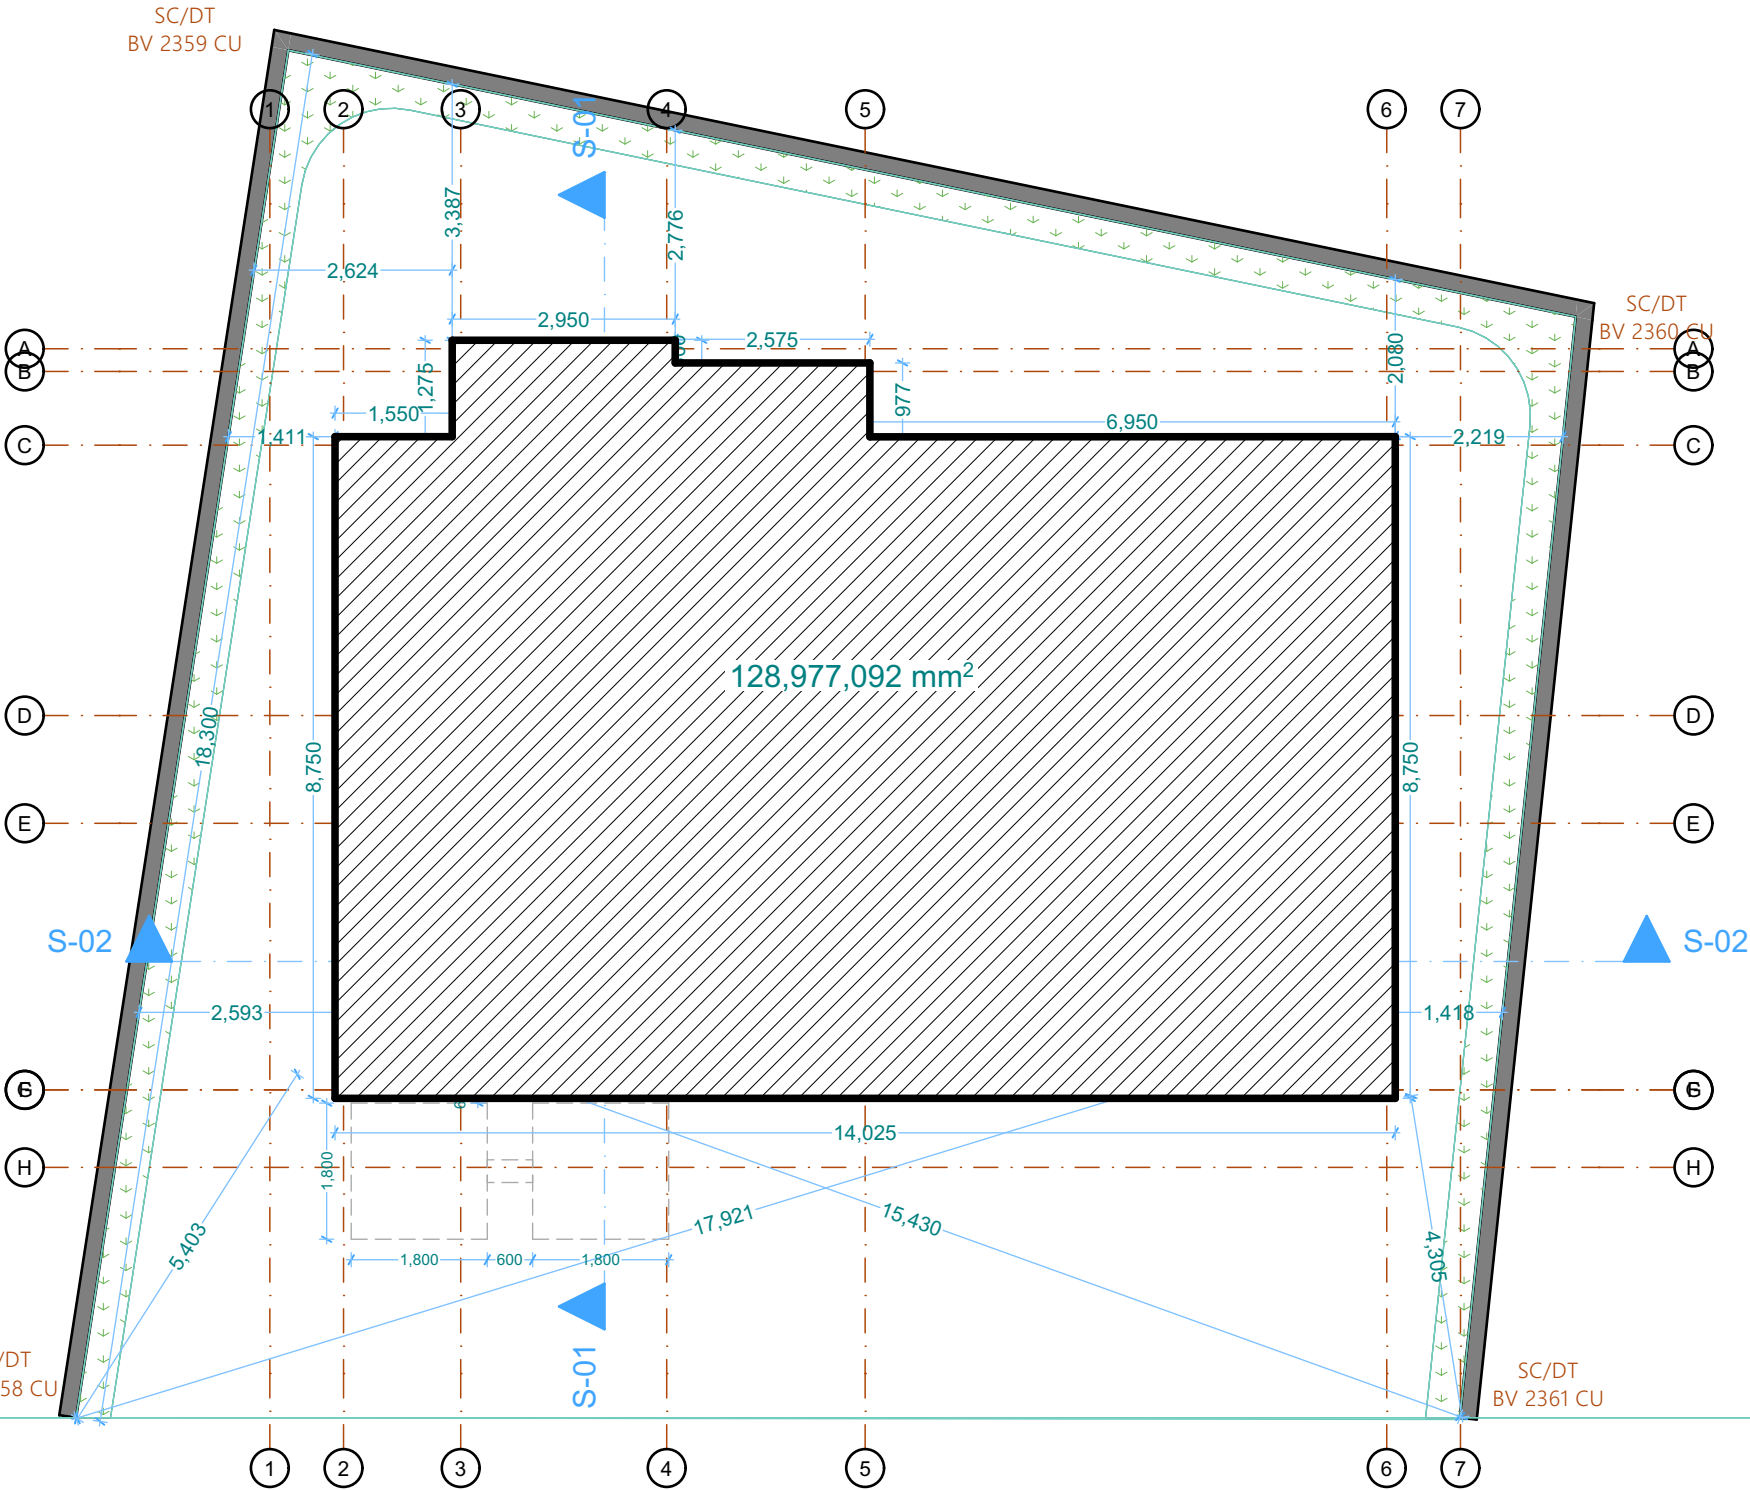

EXISTING ROAD



Front Point Properties & Construction
(Design)

PROJECT TITLE	
PROPOSED RESIDENTIAL DEVELOPMENT	
PROJECT OWNER	JONATHAN MIRACLE
LOCATION	Lucas extension, Abraka, Ethiope East LGA, Delta state



DESIGNED		REVISIONS		
		NO	DATE	REMARKS
CHECKED				
DRAWN				
SCALE:	Dimensions should be read			

CONSULTANTS
Front Point Properties & Construction(Design) +2349030763071, +2348112345047 GBS Architects(Visualization)

SHEET CONTENTS	SHEET NO.
Site Plan	3
ALL DIMENSIONS SHALL BE VERIFIED ON SITE BEFORE COMMENCING ANY WORK. ANY DISCREPANCIES OCCURRING IN THIS DRAWING MUST BE REFERRED TO THE ARCHITECT, ENGINEER, OR PROJECT IN CHARGE BEFORE COMMENCING ANY WORK.	

Ground Floor Plan

Front Point Properties & Construction (Design)

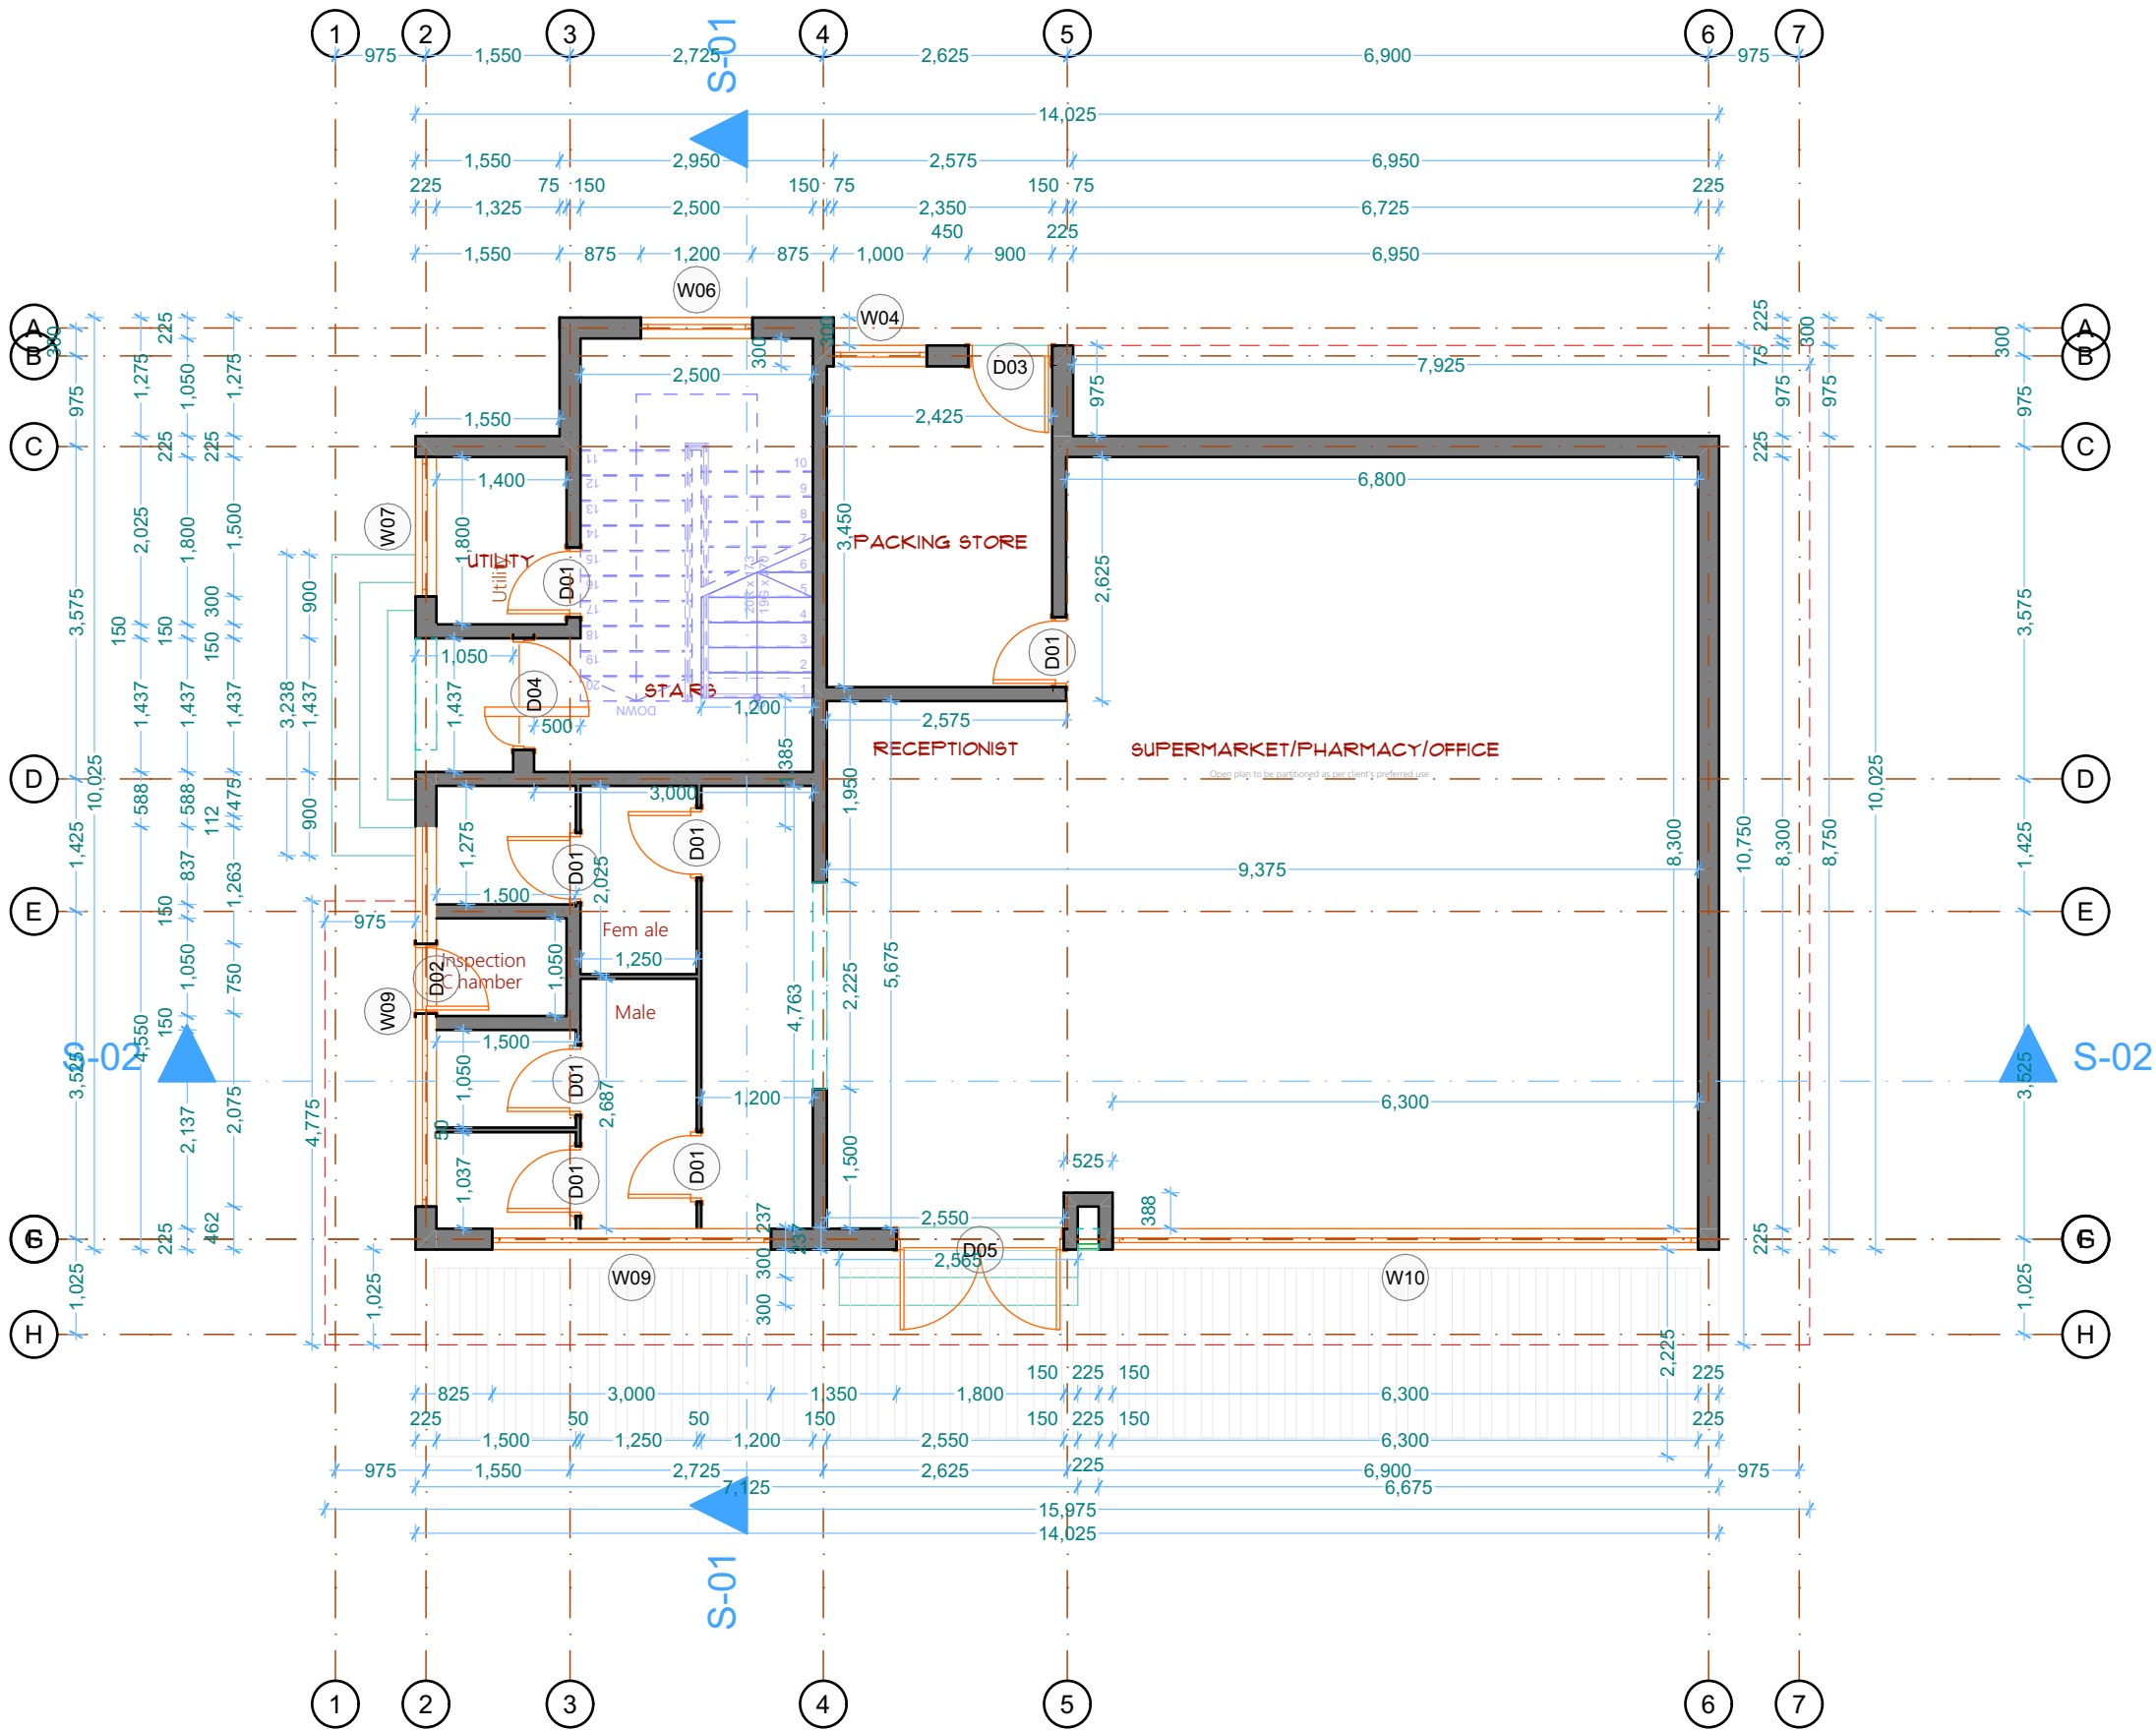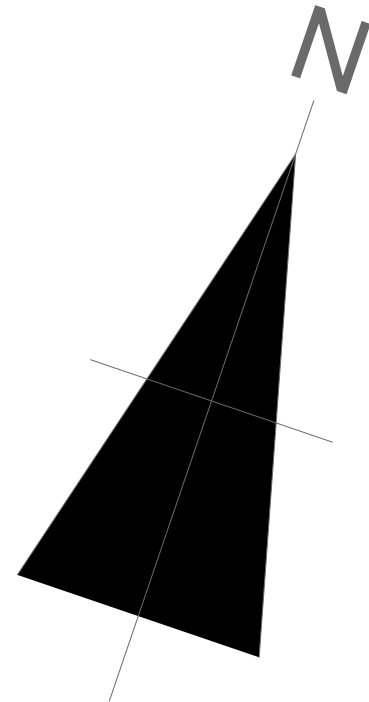

GENERAL NOTES

Drawing Interpretation:
All dimensions are in millimeters (mm) unless otherwise noted.
Discrepancies between drawings shall be reported to the architect for clarification.

Drawing Revisions:
Always refer to the latest revision. Obsolete drawings must not be used.

Coordination:
All disciplines (Architectural, Structural, MEP) must be cross-referenced for conflicts.
Report clashes between services (e.g., ductwork vs. structural beams) immediately.

Site Verification:
Contractor must verify all dimensions on-site before construction.

ARCHITECTURAL

All finishes shall be as per the Finishes Schedule and Material Specifications.
Mock-ups of critical finishes (e.g., façade, flooring) must be approved before full installation.

Compliance:
Construction shall comply with local building codes, accessibility standards (e.g., ADA/ANSI), and fire regulations.

Tolerances:
Construction tolerances shall not exceed ±5mm unless otherwise specified.

STRUCTURAL

Design Standards:
Concrete, steel, and reinforcement shall comply with ACI 318, AISC, or local codes.

Loads:
All dead/live loads are as per ASCE 7 (or relevant standard). Unauthorized additional loads are prohibited.

Reinforcement:
Bar bending schedules (BBS) must be approved before fabrication.

SANITARY

Piping:
Use PVC/CPVC/GI as specified. Slope for drainage pipes: 2% minimum.

Water Supply:
Pressure test all pipes at 1.5× working pressure before concealment.

Fixtures:
Locations are indicative; confirm with architectural layouts.

Grease Traps & Interceptors:
Install as per local sanitary codes.

ELECTRICAL

Standards:
Installation shall comply with NEC/IEC (or local electrical code).

Coordination:
Conduits and cable trays must avoid clashes with plumbing/mechanical ducts.

Fixtures:
Lighting layouts are schematic; final positions to be confirmed with architect.

Earthing & Safety:
All systems must include proper grounding and surge protection.

MECHANICAL

Ductwork:
Install as per SMACNA standards. Fire dampers required at rated walls.

Equipment:
AHUs, chillers, and fans shall be as per manufacturer's specifications.

Insulation:
All ductwork in unconditioned spaces must be insulated.



Front Point Properties & Construction
(Design)

PROJECT TITLE	
PROPOSED RESIDENTIAL DEVELOPMENT	
PROJECT OWNER	JONATHAN MIRACLE
LOCATION	Lucas extension, Abraka, Ethiope East LGA, Delta state

DESIGNED	REVISIONS		
	NO	DATE	REMARKS
CHECKED			
DRAWN			
SCALE:	Dimensions should be read		

CONSULTANTS
Front Point Properties & Construction(Design) +2349030763071, +2348112345047
GBS Architects(Visualization)

SHEET CONTENTS	SHEET NO.
Ground Floor Plan	4
ALL DIMENSIONS SHALL BE VERIFIED ON SITE BEFORE COMMENCING ANY WORK. ANY DISCREPANCIES OCCURRING IN THIS DRAWING MUST BE REFERRED TO THE ARCHITECT, ENGINEER, OR PROJECT-IN-CHARGE BEFORE COMMENCING ANY WORK.	

First Floor Plan

Front Point Properties & Construction (Design)

GENERAL NOTES

- Drawing Interpretation:**
All dimensions are in millimeters (mm) unless otherwise noted.
Discrepancies between drawings shall be reported to the architect for clarification.
- Drawing Revisions:**
Always refer to the latest revision. Obsolete drawings must not be used.
- Coordination:**
All disciplines (Architectural, Structural, MEP) must be cross-referenced for conflicts.
Report clashes between services (e.g., ductwork vs. structural beams) immediately.
- Site Verification:**
Contractor must verify all dimensions on-site before construction.

ARCHITECTURAL

- All finishes shall be as per the Finishes Schedule and Material Specifications.
Mock-ups of critical finishes (e.g., façade, flooring) must be approved before full installation.
- Compliance:**
Construction shall comply with local building codes, accessibility standards (e.g., ADA/ANSI), and fire regulations.
- Tolerances:**
Construction tolerances shall not exceed ±5mm unless otherwise specified.

STRUCTURAL

- Design Standards:**
Concrete, steel, and reinforcement shall comply with ACI 318, AISI, or local codes.
- Loads:**
All dead/live loads are as per ASCE 7 (or relevant standard). Unauthorized additional loads are prohibited.
- Reinforcement:**
Bar bending schedules (BBS) must be approved before fabrication.

SANITARY


- Piping:**
Use PVC/CPVC/GI as specified. Slope for drainage pipes: 2% minimum.
- Water Supply:**
Pressure test all pipes at 1.5× working pressure before concealment.
- Fixtures:**
Locations are indicative; confirm with architectural layouts.
- Grease Traps & Interceptors:**
Install as per local sanitary codes.

ELECTRICAL

- Standards:**
Installation shall comply with NEC/IEC (or local electrical code).
- Coordination:**
Conduits and cable trays must avoid clashes with plumbing/mechanical ducts.
- Fixtures:**
Lighting layouts are schematic; final positions to be confirmed with architect.
- Earthing & Safety:**
All systems must include proper grounding and surge protection.

MECHANICAL

- Ductwork:**
Install as per SMACNA standards. Fire dampers required at rated walls.
- Equipment:**
AHUs, chillers, and fans shall be as per manufacturer's specifications.
- Insulation:**
All ductwork in unconditioned spaces must be insulated.

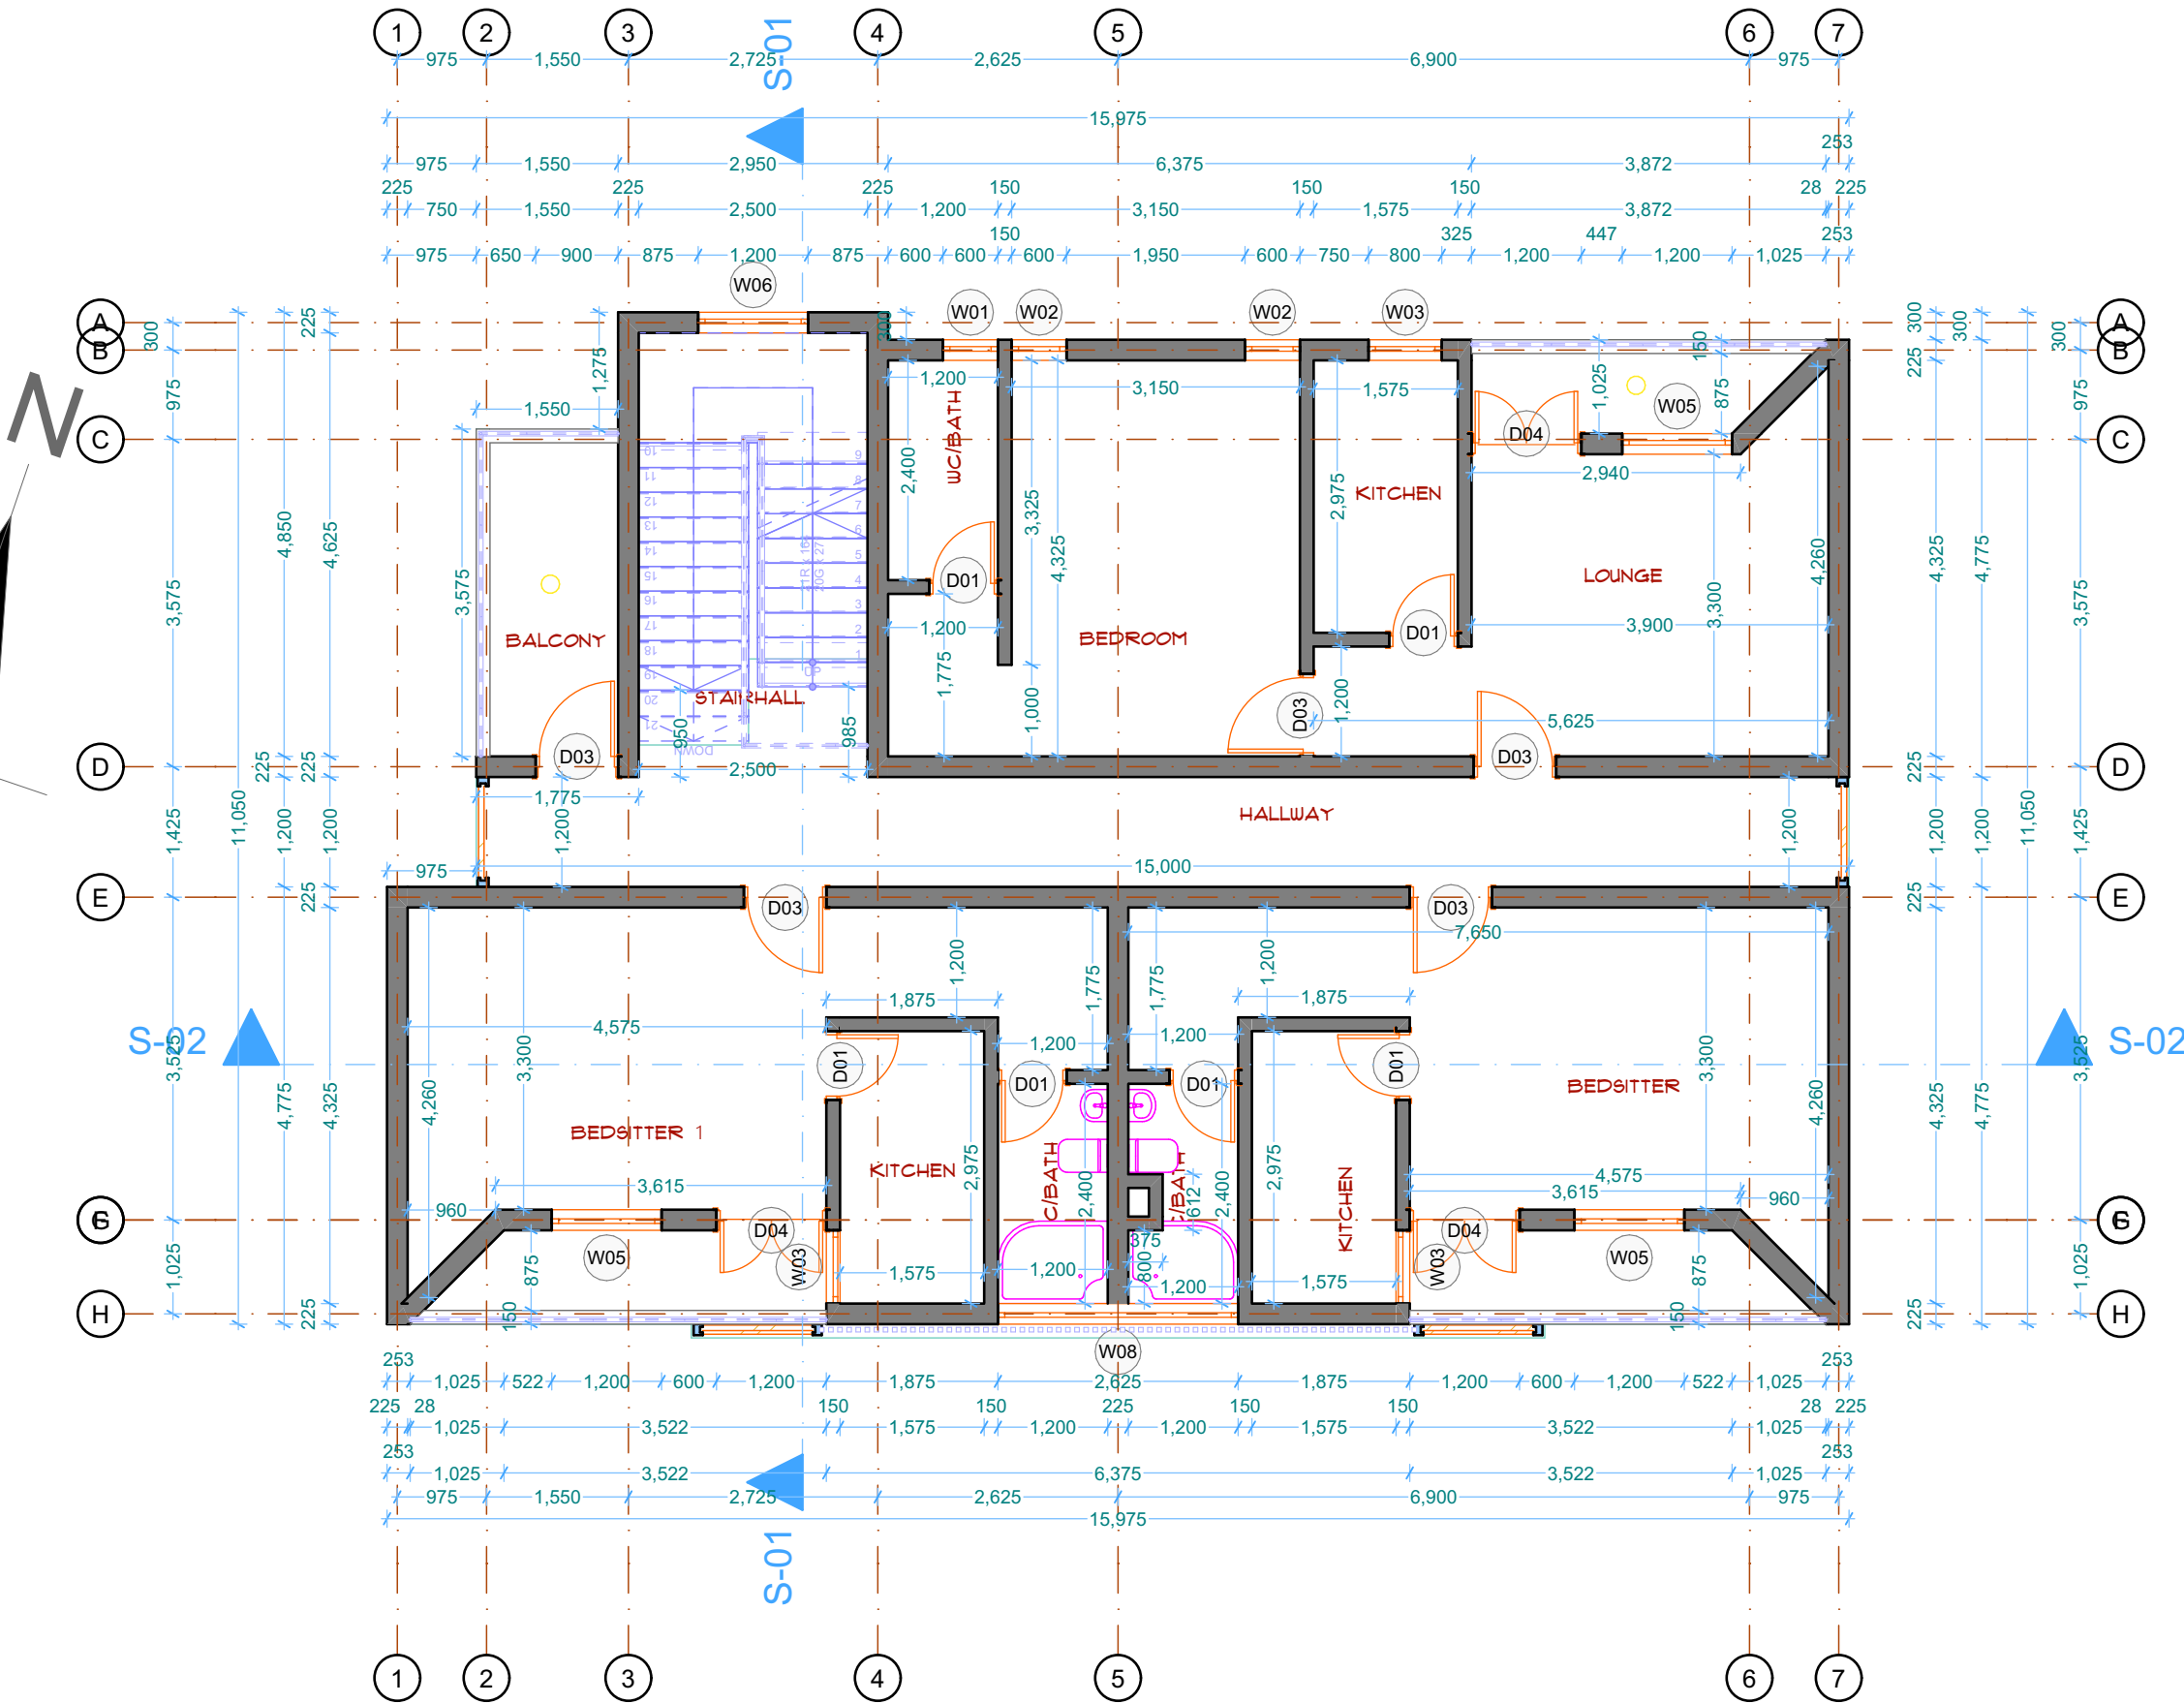

Front Point Properties & Construction
(Design)

PROJECT TITLE	
PROPOSED RESIDENTIAL DEVELOPMENT	
PROJECT OWNER	JONATHAN MIRACLE
LOCATION	Lucas extension, Abraka, Ethiope East LGA, Delta state

DESIGNED	REVISIONS		
	NO	DATE	REMARKS
CHECKED			
DRAWN			
SCALE:	Dimensions should be read		

CONSULTANTS
Front Point Properties & Construction(Design)
+2349030763071, +2348112345047
GBS Architects(Visualization)

SHEET CONTENTS	SHEET NO.
First Floor Plan	5
ALL DIMENSIONS SHALL BE VERIFIED ON SITE BEFORE COMMENCING ANY WORK. ANY DISCREPANCIES OCCURRING IN THIS DRAWING MUST BE REFERRED TO THE ARCHITECT, ENGINEER, OR PROJECT-IN-CHARGE BEFORE COMMENCING ANY WORK.	

Second Floor Plan

Front Point Properties &
Construction (Design)

GENERAL NOTES

- Drawing Interpretation:**
All dimensions are in millimeters (mm) unless otherwise noted.
Discrepancies between drawings shall be reported to the architect for clarification.
- Drawing Revisions:**
Always refer to the latest revision. Obsolete drawings must not be used.
- Coordination:**
All disciplines (Architectural, Structural, MEP) must be cross-referenced for conflicts.
Report clashes between services (e.g., ductwork vs. structural beams) immediately.
- Site Verification:**
Contractor must verify all dimensions on-site before construction.

ARCHITECTURAL

- All finishes shall be as per the Finishes Schedule and Material Specifications.
Mock-ups of critical finishes (e.g., façade, flooring) must be approved before full installation.
- Compliance:**
Construction shall comply with local building codes, accessibility standards (e.g., ADA/ANSI), and fire regulations.
- Tolerances:**
Construction tolerances shall not exceed ±5mm unless otherwise specified.

STRUCTURAL

- Design Standards:**
Concrete, steel, and reinforcement shall comply with ACI 318, AISI, or local codes.
- Loads:**
All dead/live loads are as per ASCE 7 (or relevant standard). Unauthorized additional loads are prohibited.
- Reinforcement:**
Bar bending schedules (BBS) must be approved before fabrication.

SANITARY


- Piping:**
Use PVC/CPVC/GI as specified. Slope for drainage pipes: 2% minimum.
- Water Supply:**
Pressure test all pipes at 1.5× working pressure before concealment.
- Fixtures:**
Locations are indicative; confirm with architectural layouts.
- Grease Traps & Interceptors:**
Install as per local sanitary codes.

ELECTRICAL

- Standards:**
Installation shall comply with NEC/IEC (or local electrical code).
- Coordination:**
Conduits and cable trays must avoid clashes with plumbing/mechanical ducts.
- Fixtures:**
Lighting layouts are schematic; final positions to be confirmed with architect.
- Earthing & Safety:**
All systems must include proper grounding and surge protection.

MECHANICAL

- Ductwork:**
Install as per SMACNA standards. Fire dampers required at rated walls.
- Equipment:**
AHUs, chillers, and fans shall be as per manufacturer's specifications.
- Insulation:**
All ductwork in unconditioned spaces must be insulated.

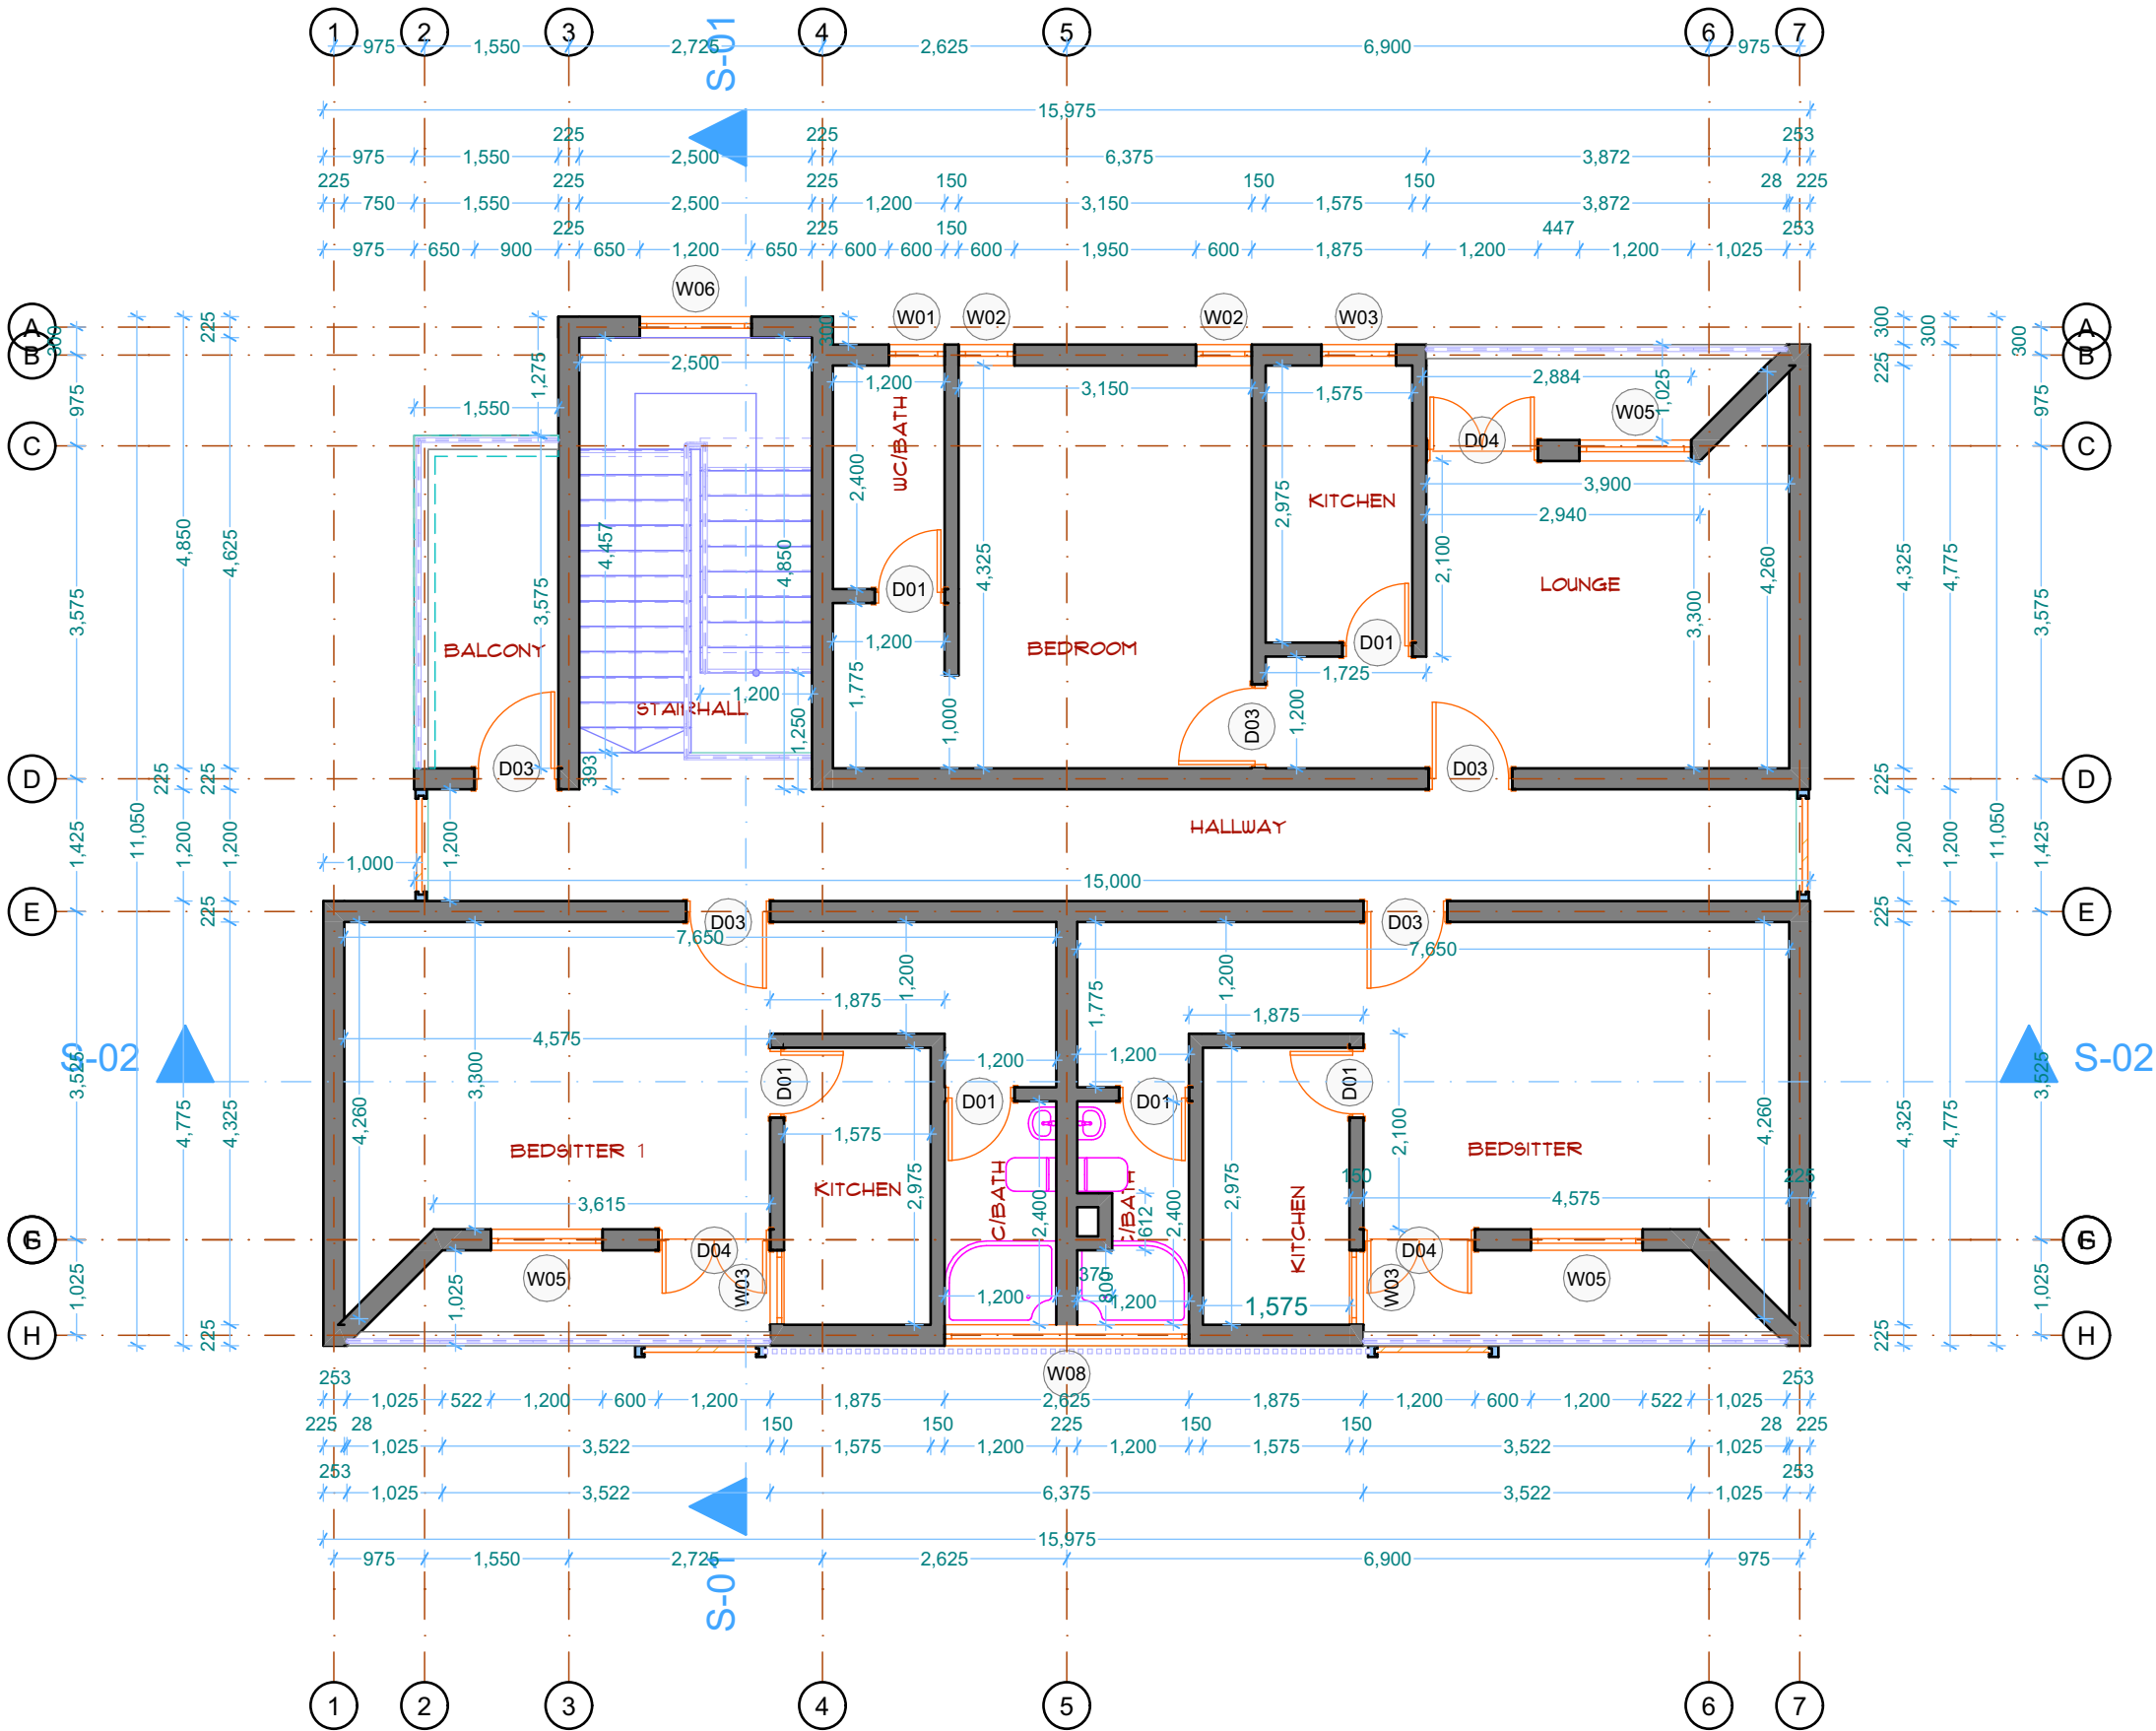

Front Point Properties & Construction
(Design)

PROJECT TITLE	
PROPOSED RESIDENTIAL DEVELOPMENT	
PROJECT OWNER	JONATHAN MIRACLE
LOCATION	Lucas extension, Abraka, Ethiope East LGA, Delta state

ALL DIMENSIONS SHALL BE VERIFIED ON SITE BEFORE COMMENCING ANY WORK.
ANY DISCREPANCIES OCCURRING IN THIS DRAWING MUST BE REFERRED TO THE ARCHITECT, ENGINEER,
OR PROJECT-IN-CHARGE BEFORE COMMENCING ANY WORK.